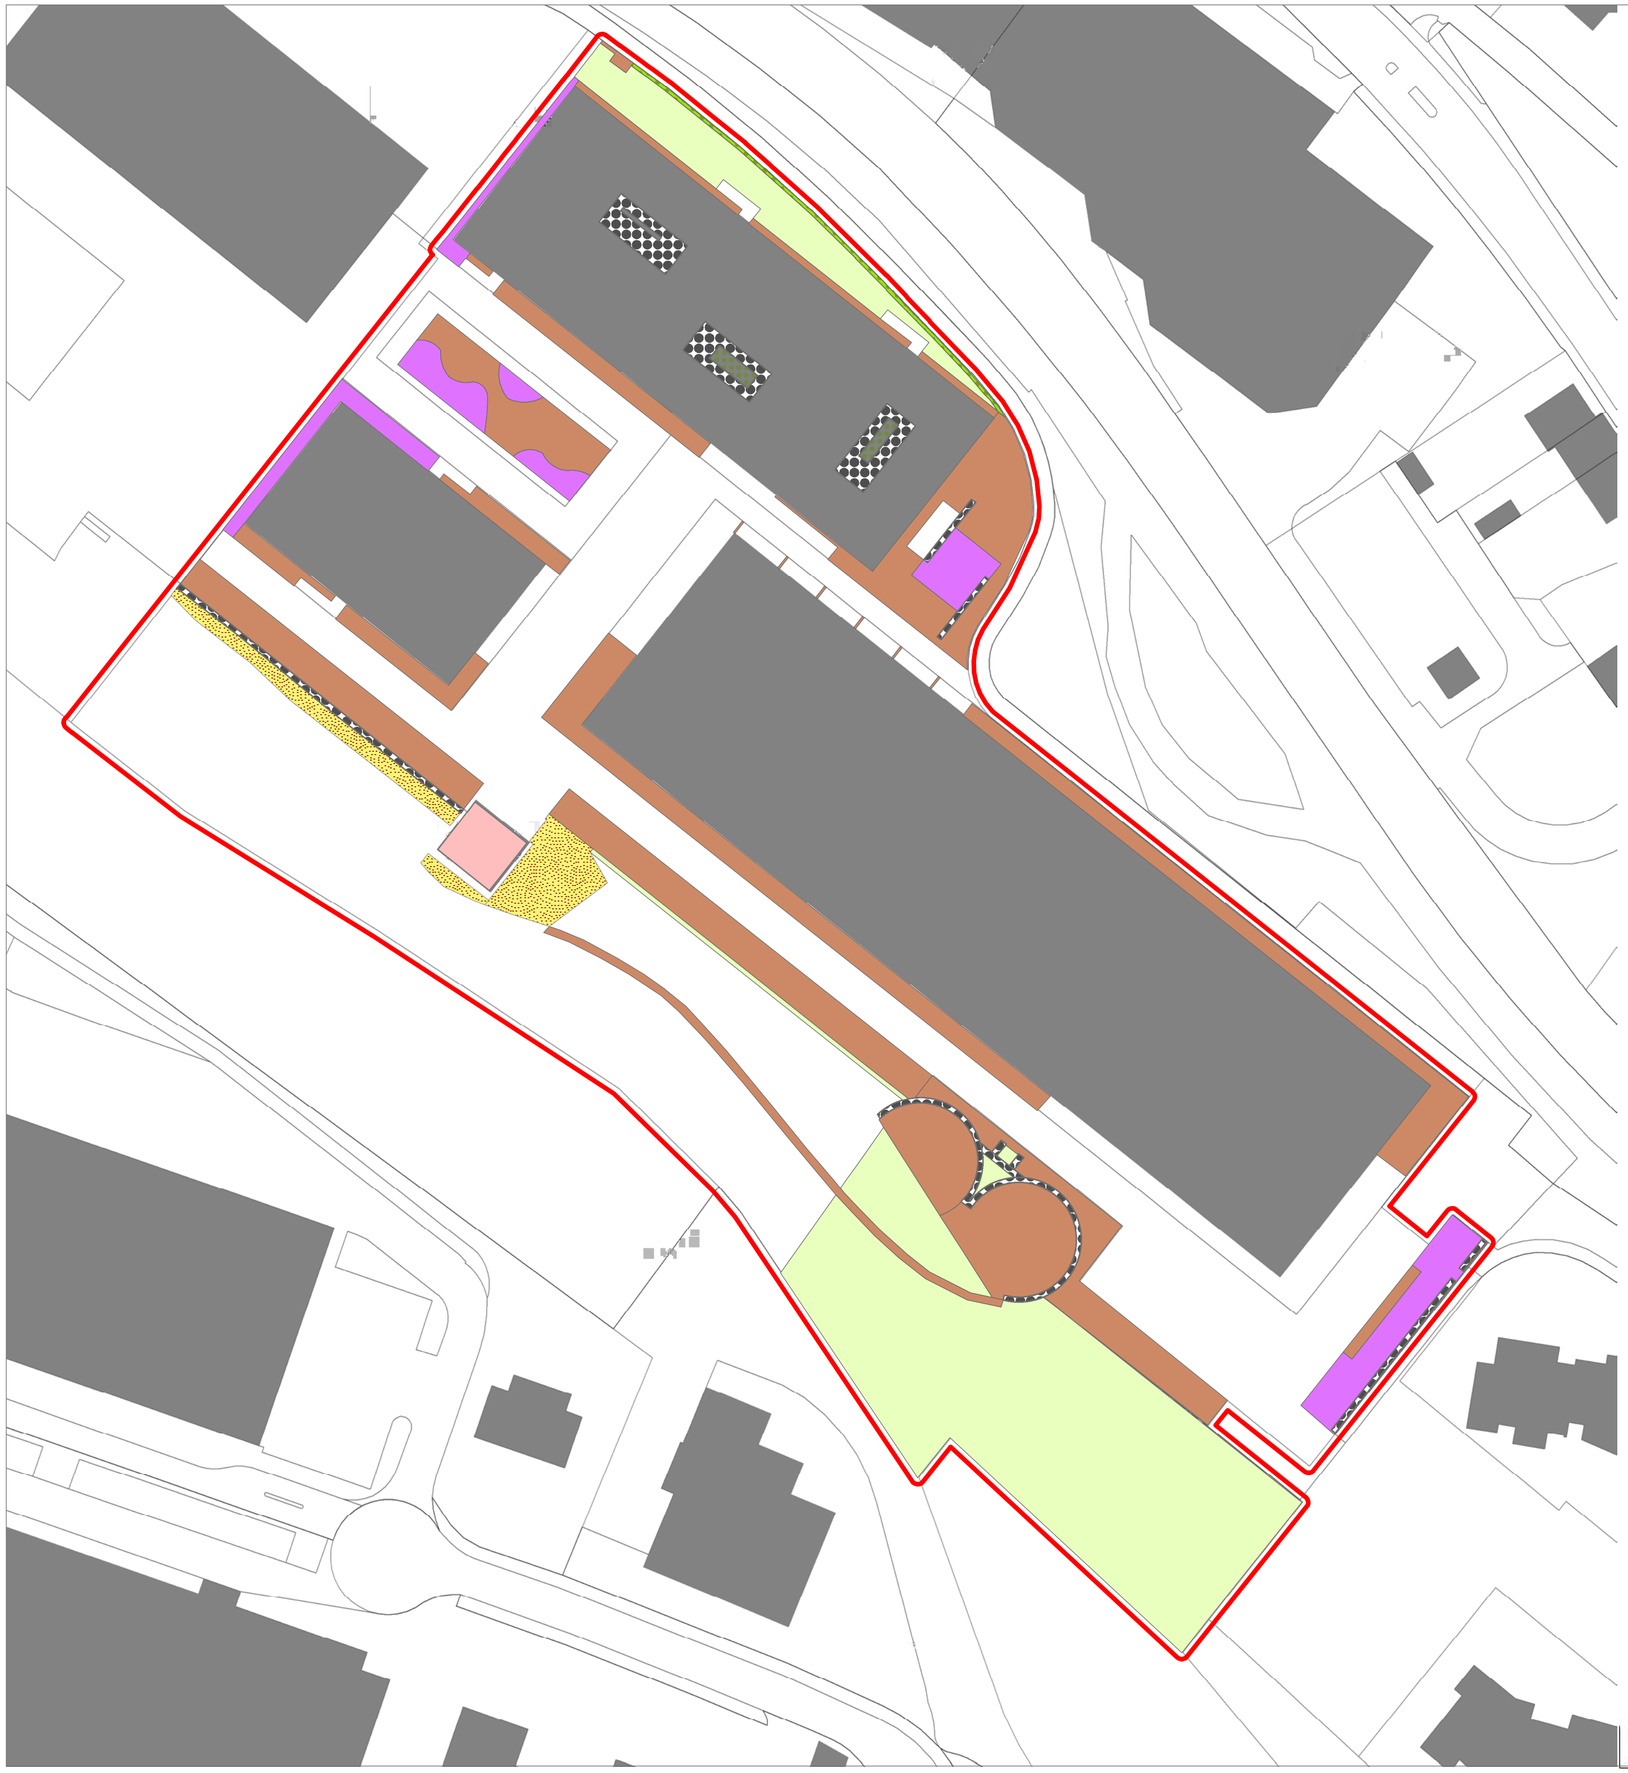

Legende

Objekt

Rasen
- Geb.Rasen kf.
- Blumenrasen

Wiesen
- Feuchtwiese
- Blumenwiese gf.
- Blumenwiese kf.
- Magerrasen
- Saumvegetation

Rabatten
- Wechselflor
- Moorbeet
- Stauden. int.
- Stauden. ext.
- Beetrosen
- Ruderalfläche

Hecken
- Wildhecke
- Formhecke + 1.5 m
- Formhecke - 1.5 m

Gehölzflächen
- Gehölz & Bodend.
- Bodendecker
- Gehölzrabatte
- Wald

Spezielle Bepflanzungsformen
- Dach: ext. Stauden

Beläge
- Asphaltbelag
- Rasengittersteine
- Holzhäckselbelag
- Chaussierung
- Betonpl./Verbund/ Naturstein
- Geröllstreifen/Bollensteine

Wasserflächen
- Brunnen
- Gewässer, ruhend

Anderes
- Anderes

Baum
- Laubb. Kopf-/Form
- Laubb. nat. kleink.
- Laubb. nat. grossk.
- Nadelb. nat.
- Hochstammobst
- Strassenb. Laub Kopf/Form
- Strassenb. Laub nat. kleink.
- Strassenb. Laub nat. grossk.

Spezielle Bepflanzungsformen
- Pflanzgefäss mobil Dauerbepflanzung
- Pflanzgefäss Wechselflor
- Schling-& Kletterpf.

Kleinstrukturen
- Asthaufen
- Steinhaufen
- Wildbienenhotel
- Baumstämme

N

0 5 10 20 30 40 m

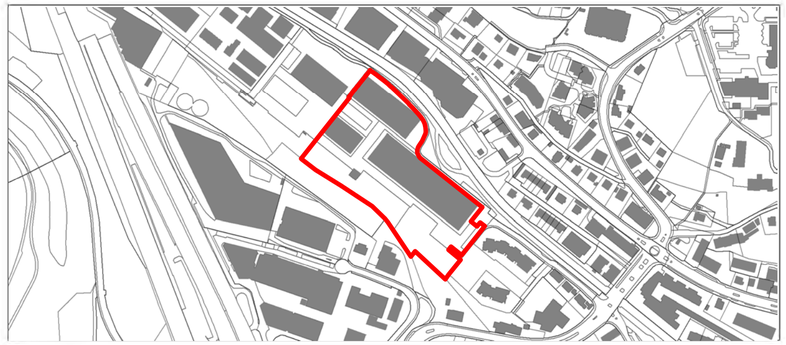

INDEX	BESCHREIBUNG	DATUM	PLANNR.	DATUM
ES	Anpassungen	13.01.2025		
ES	Ergänzung Bäume	21.08.2023		
ES	Anpassungen	30.3.2023		

REVISIONSDATEN: BASISDATEN:

1602.GR
Mühlestrasse 2-6 Ittigen
Grünflächen

Umgebungsplan

BEWIRTSCHAFTUNG / SITUATION

Umgebung

PLANNUMMER: 1602.--.0.E--.6U1

PLANVERFASSER:	DATUM ERSTELLT:	MASSSTAB:	PLANFORMAT:
MN	15.05.2020	1:650	59.4/42.0

GESAMTLEITER:

nateco

nateco AG
Sissacherstrasse 20, Postfach
CH-4460 Gelterkinden

Telefon +41 (0)61 985 44 40

nateco@nateco.ch
www.nateco.ch

Schweizerische Eidgenossenschaft
Confédération suisse
Confederazione Svizzera
Confederaziun svizra

Eidgenössisches Finanzdepartement EFD
Bundesamt für Bauten und Logistik BBL